

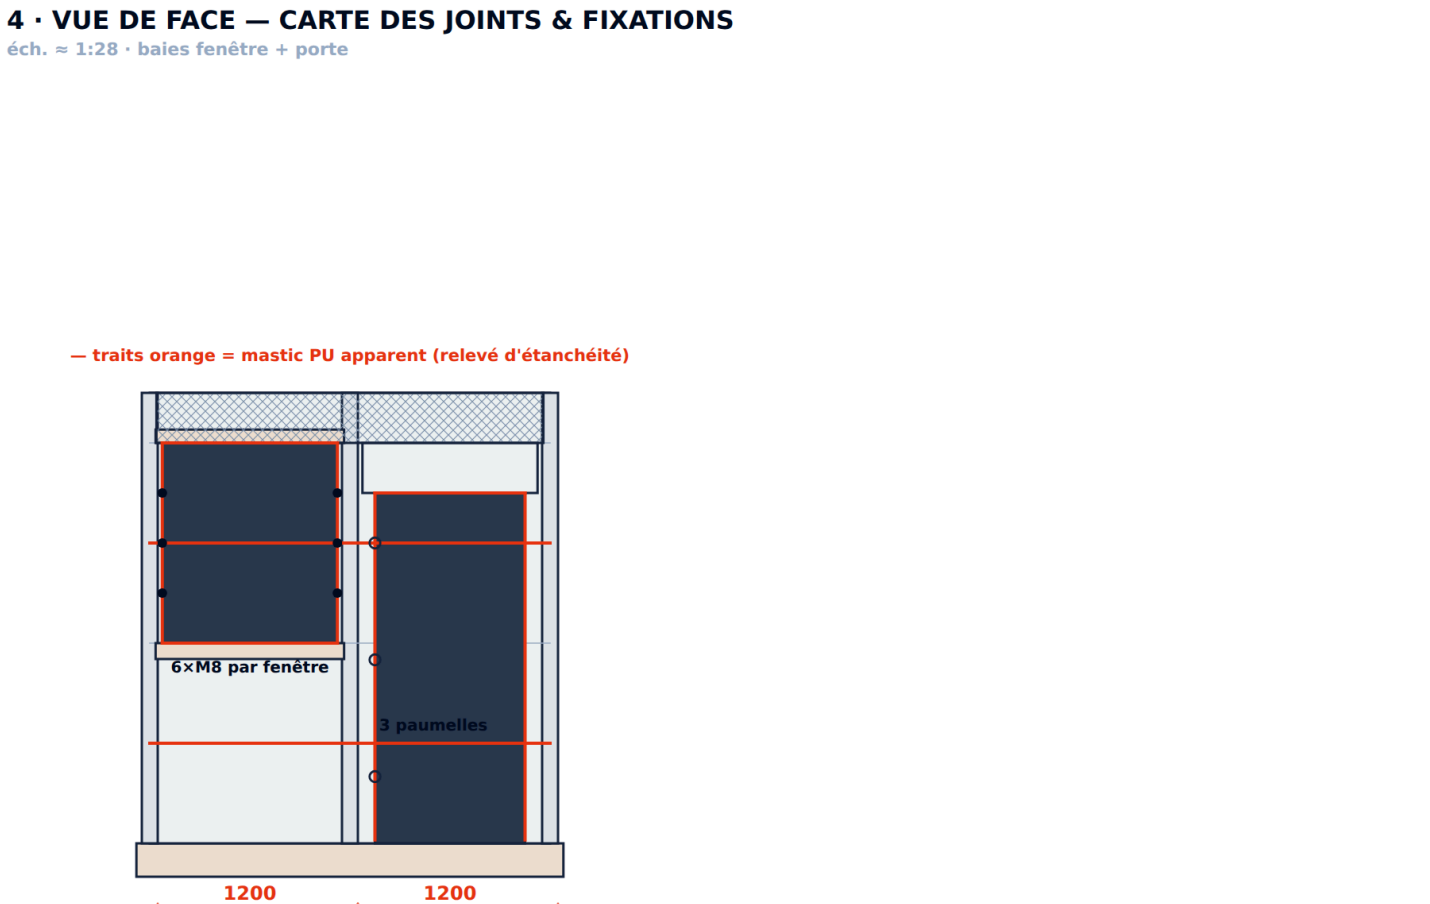
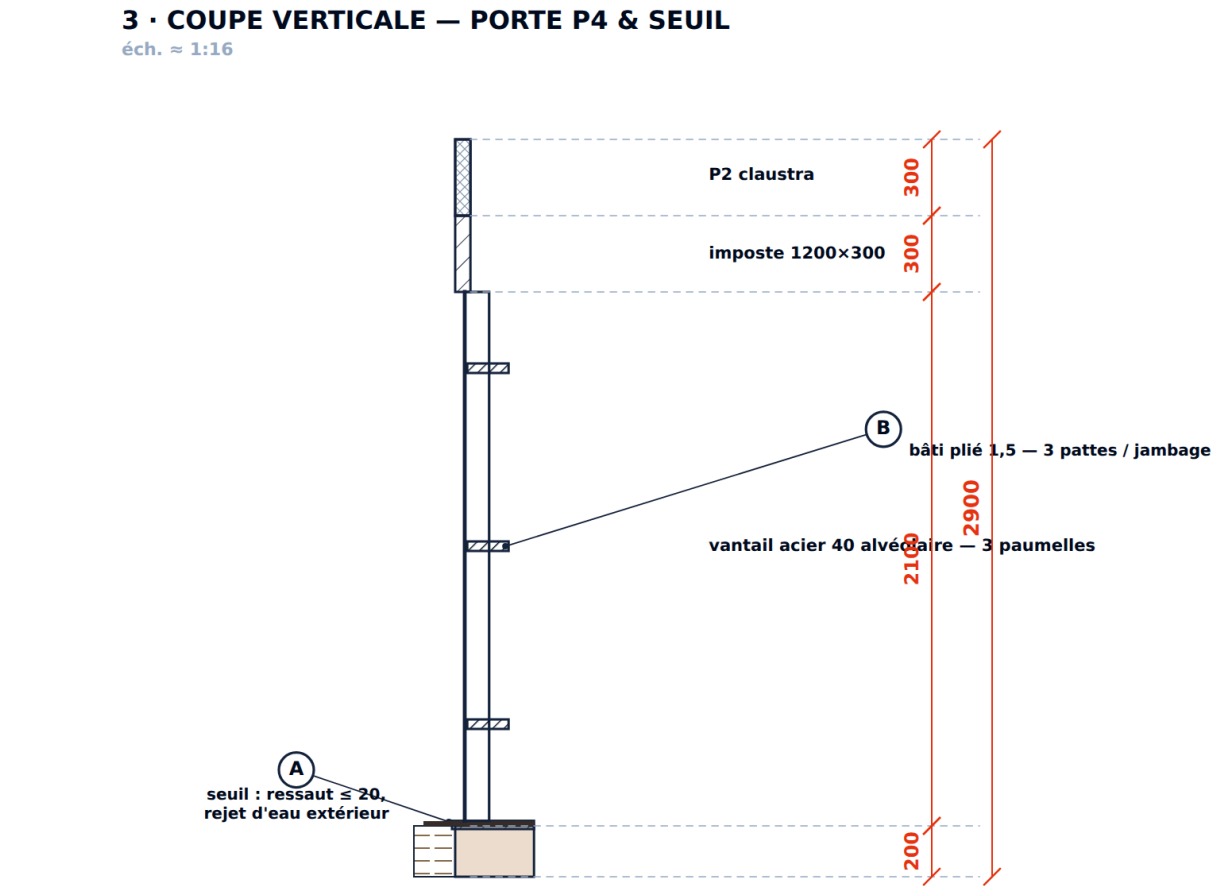
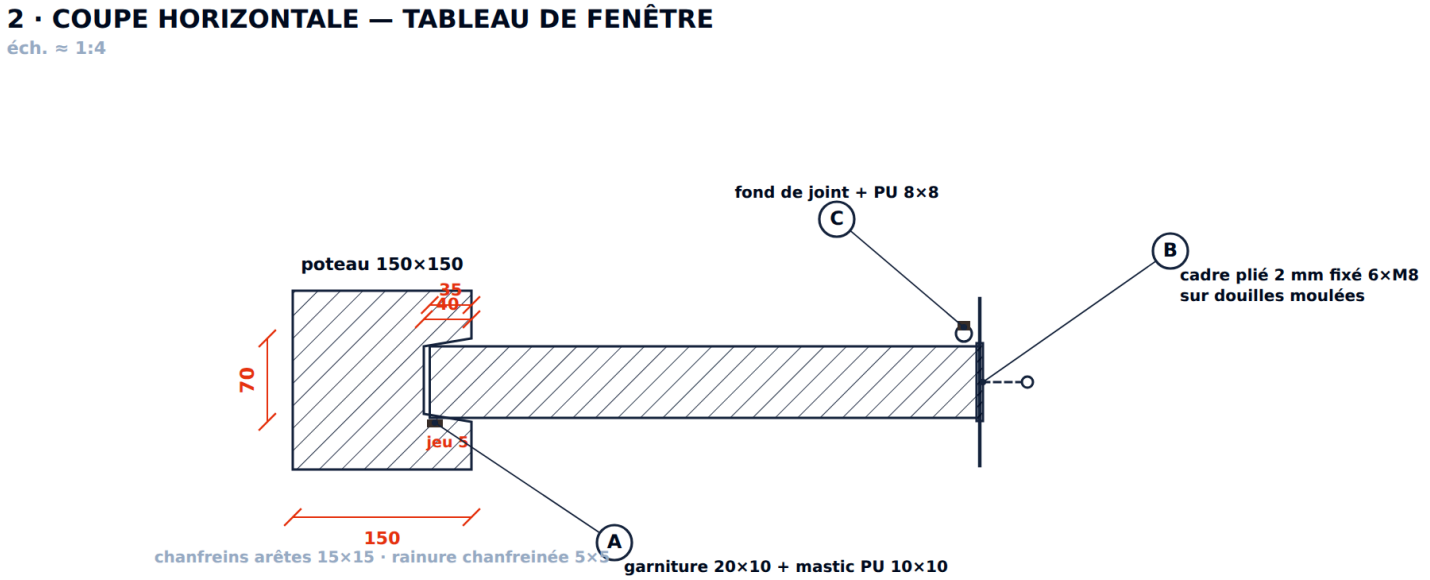


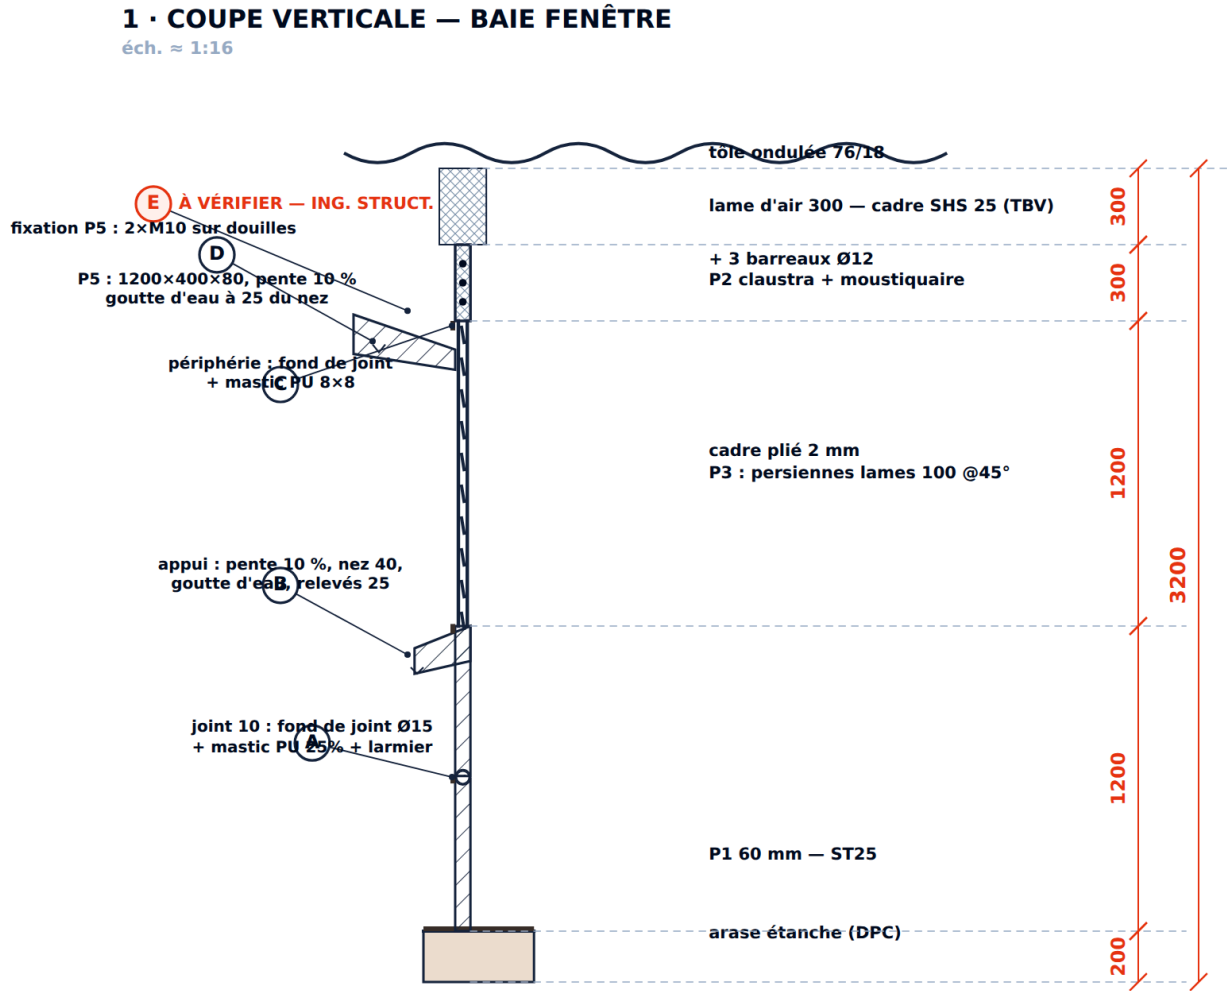


1 · COUPE — TÊTE DE POTEAU / ÉQUERRE / PANNE

éch. ≈ 1:6

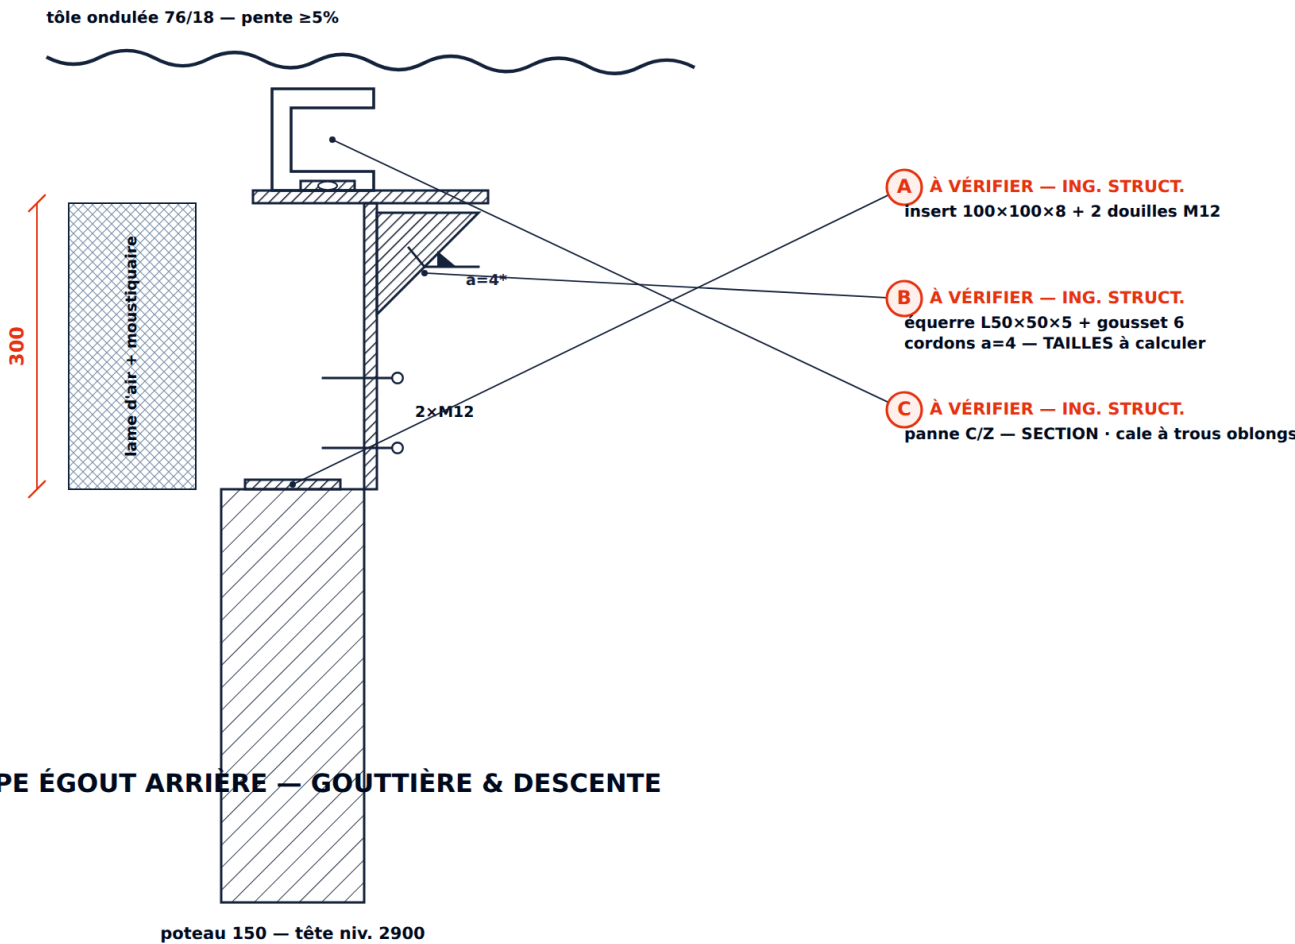


3 · COUPE ÉGOUT ARRIÈRE — GOUTTIÈRE & DESCENTE

éch. ≈ 1:8

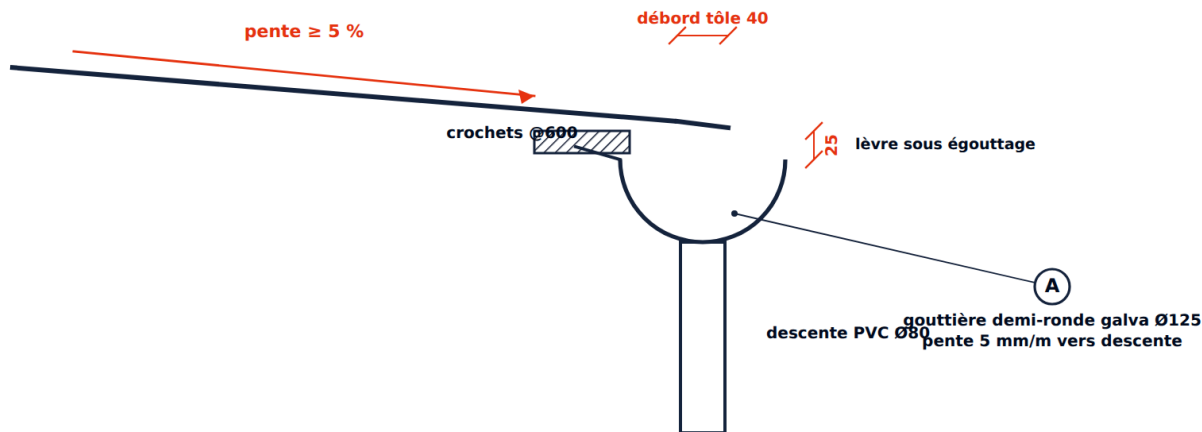


2 · FIXATION TÔLE — VIS EPDM & DENSITÉS

éch. ≈ 1:2 / schéma

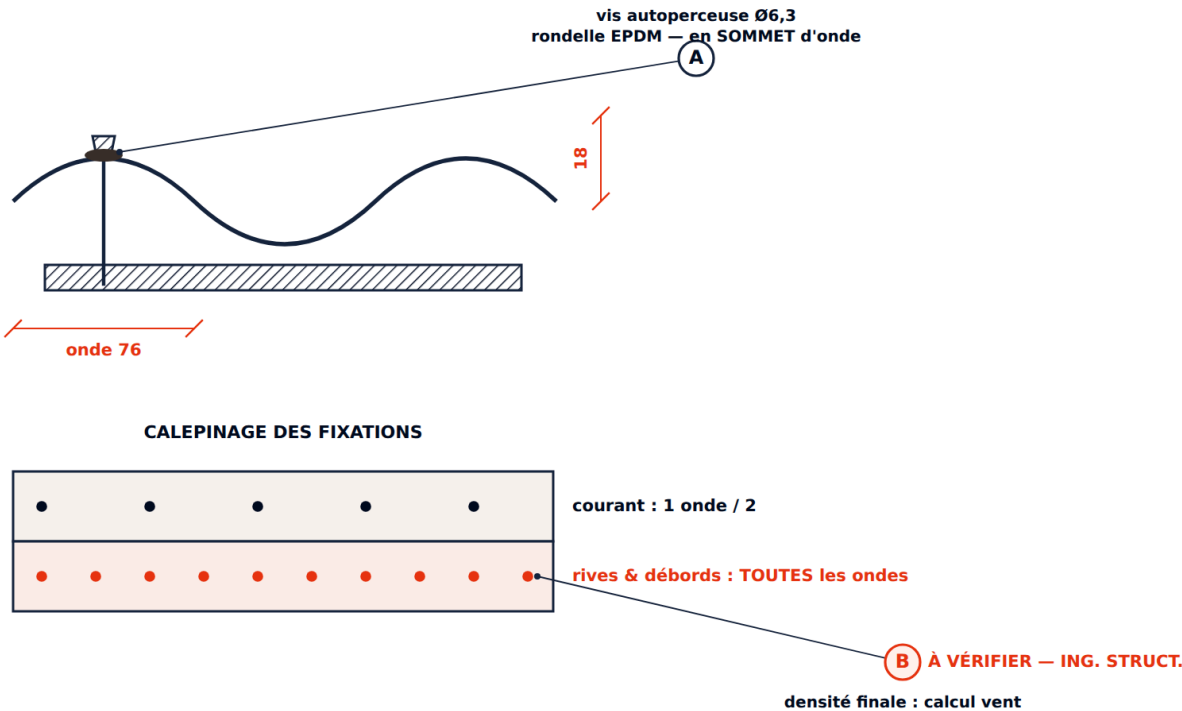


4 · PLAN DE TOITURE — ÉQUERRES, PANNES, ZONES DE FIXATION

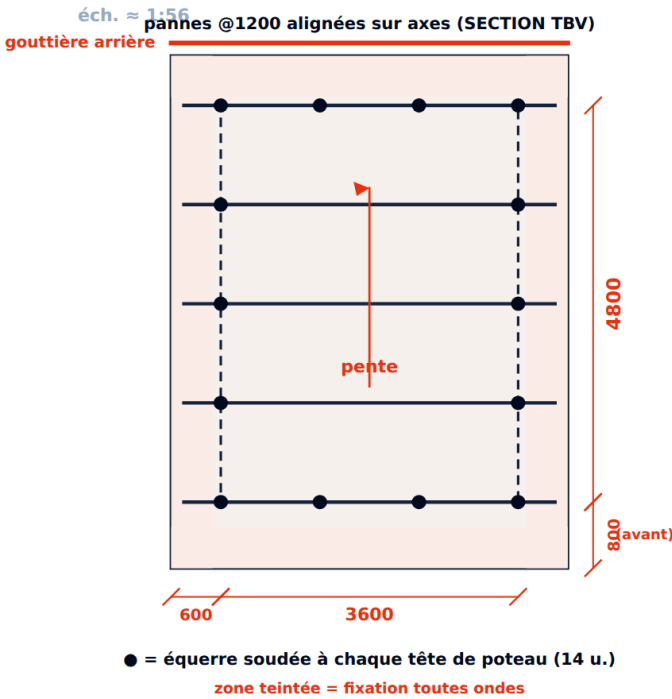


1 · COUPE HORIZONTALE — POTEAU RAINURÉ + 2 PANNEAUX

éch. ≈ 1:3

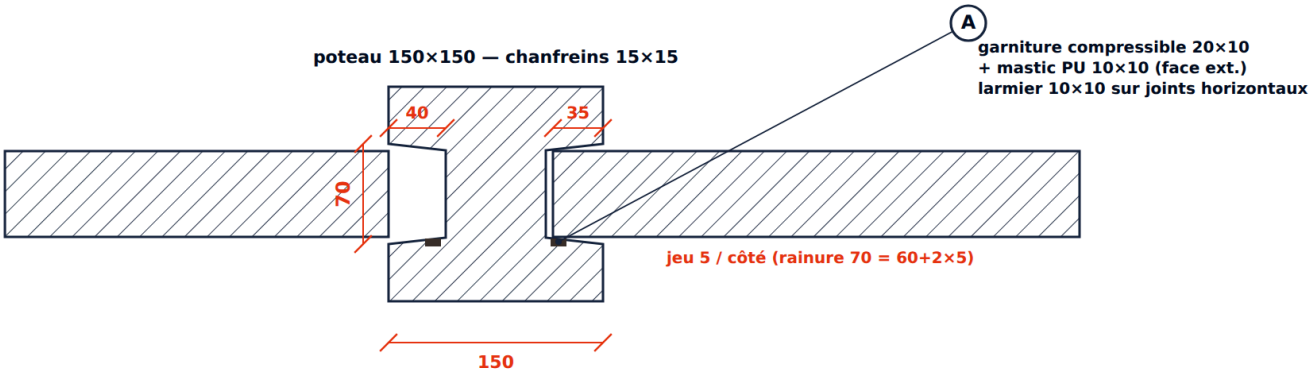

2 · COUPE VERTICALE — LINTEAU P9 SUR APPUIS + COFFRE RIDEAU

éch. ≈ 1:13

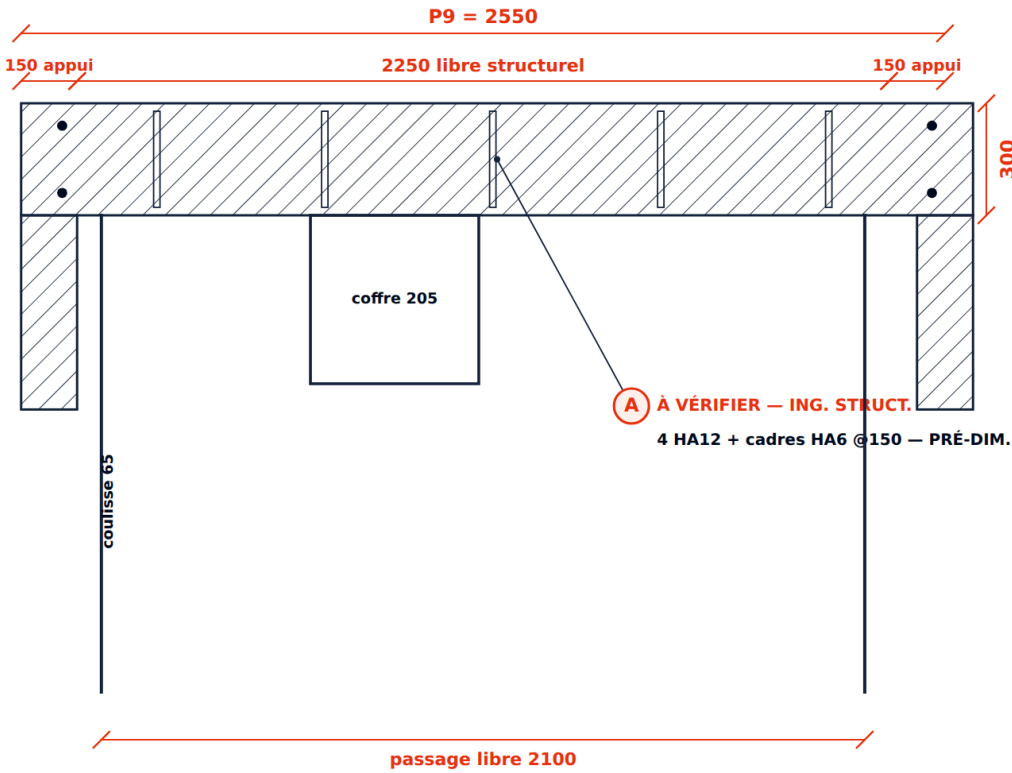


masse P9 ≈ 275 kg — méthode de pose À VÉRIFIER (pose à 6 ou levage léger)

3 · BASE VARIANTE LOCATION — SKID DÉMONTABLE


éch. ≈ 1:9

5 traverses (1 par ligne de poteaux) + 2 longerons — ensemble DÉMONTABLE

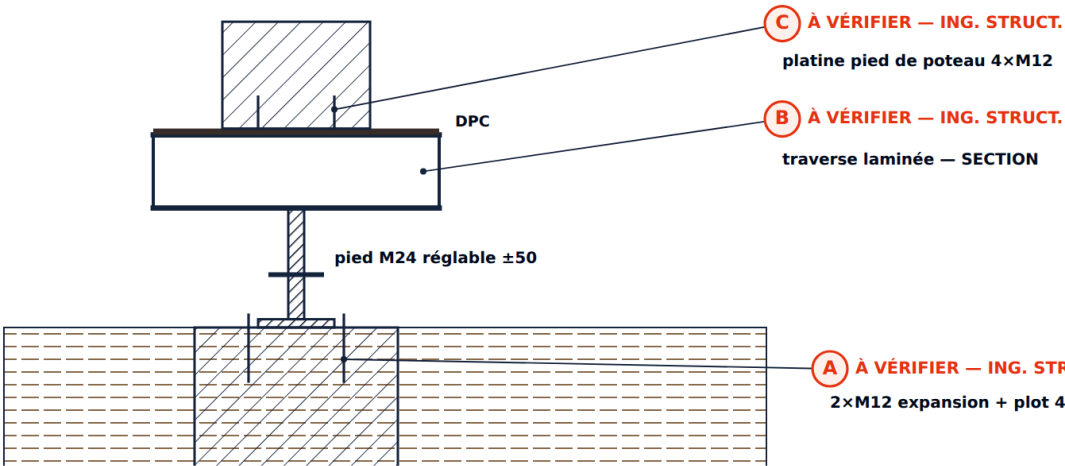

4 · BASE VARIANTE VENDU — SCÉLLEMENT + DALLE


éch. ≈ 1:9

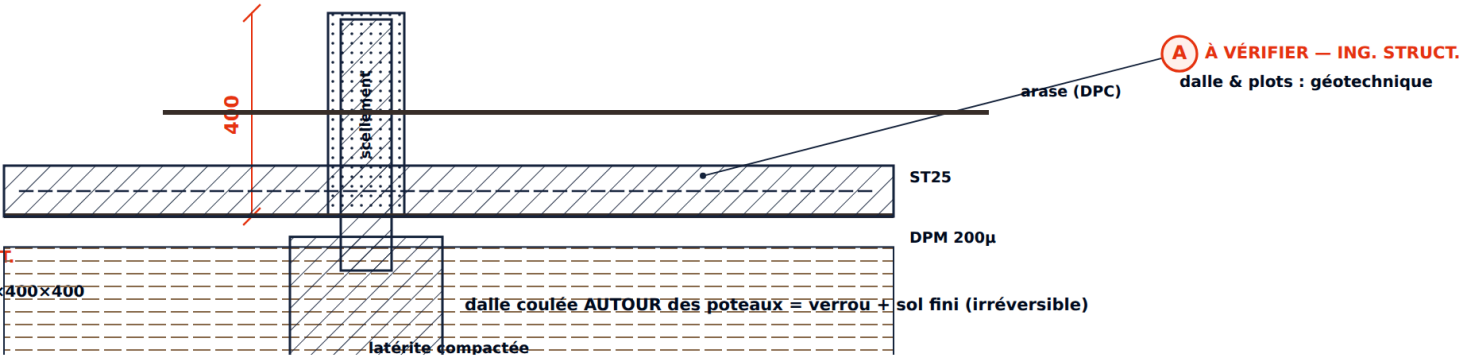


NOMENCLATURE P1→P9

P1	1200×600×60	104 kg	béton C25/30 + ST25
P2	1200×300×60	32 kg	béton + moustiquaire + 3Ø12
P3	1200×1200	35 kg	persiennes acier 2 mm
P4	900×2100+imposte	55 kg	acier plié 1,5 / vantail 40
P5	1200×400×80	88 kg	béton, pente 10%
P6	600×200×60	12 kg	béton + moustiquaire
P7	1200×600	—	plafond composite (PL. ult.)
P8	kit technique	—	citerne + coffret (PL. ult.)
P9	2550×300×150	275 kg	béton armé — TBV


1 · PLAN — 2 CABINES, SIPHONS, CITERNE, PUISARD
éch. ≈ 1:22

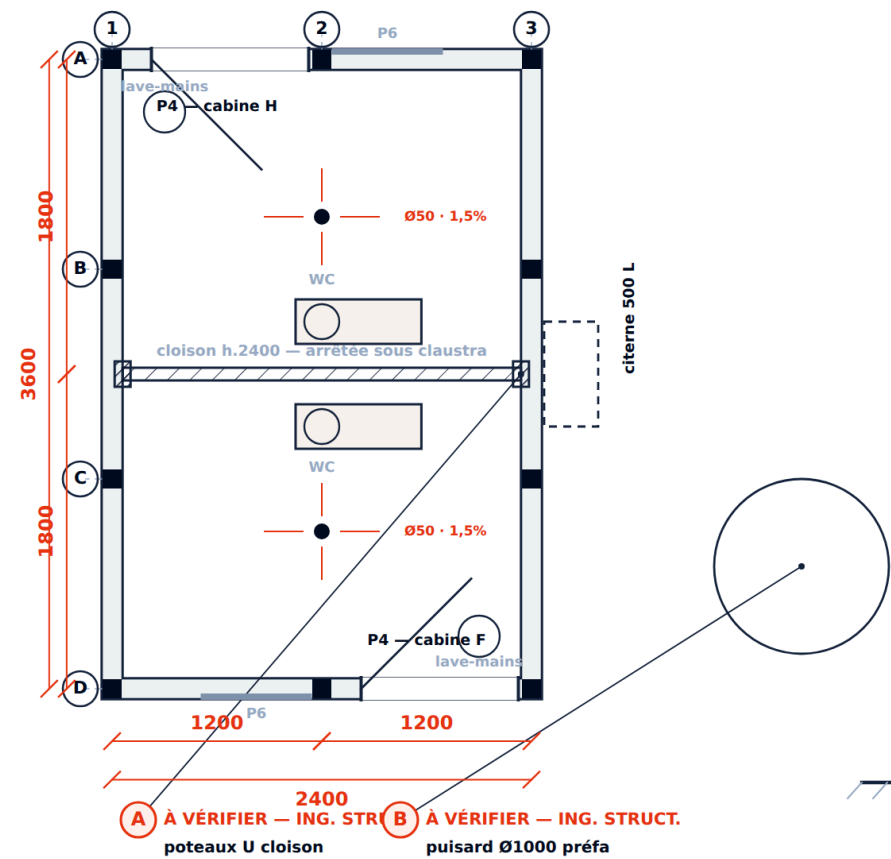


2 · ÉLÉVATION PIGNON (entrée H)
éch. ≈ 1:20

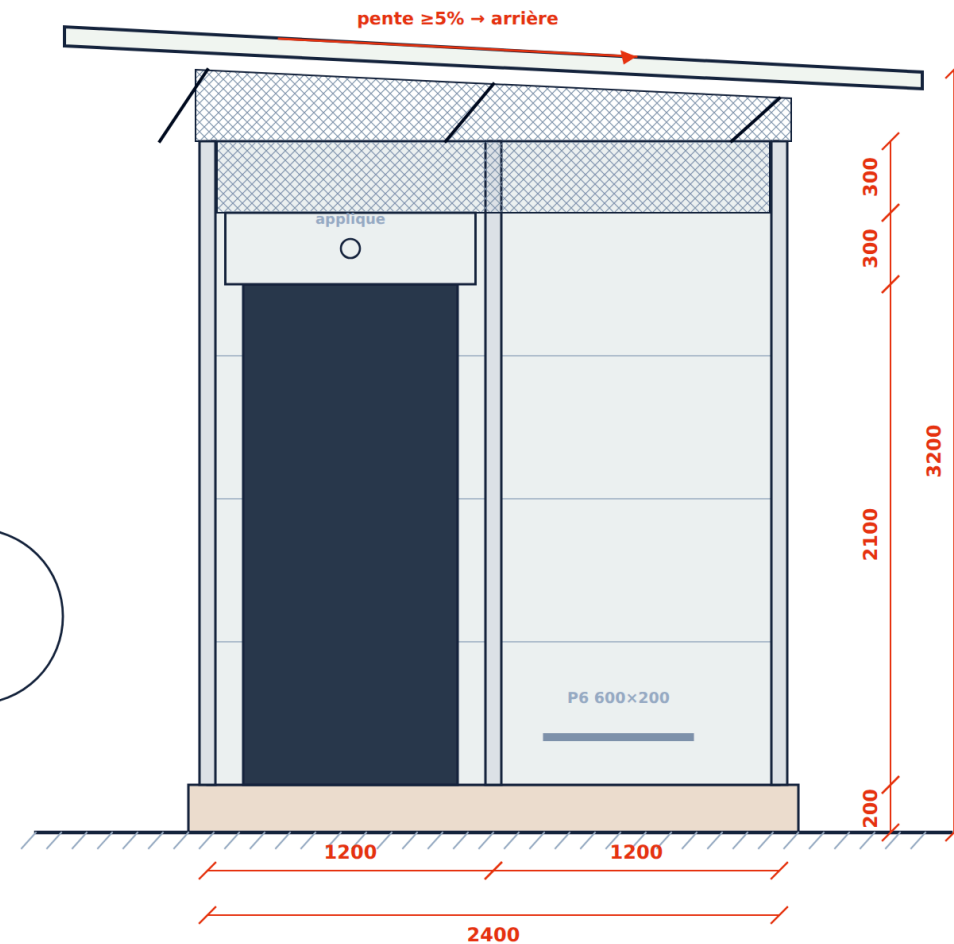

3 · ÉLÉVATION MUR LONG ARRIÈRE (côté bas)
éch. ≈ 1:24

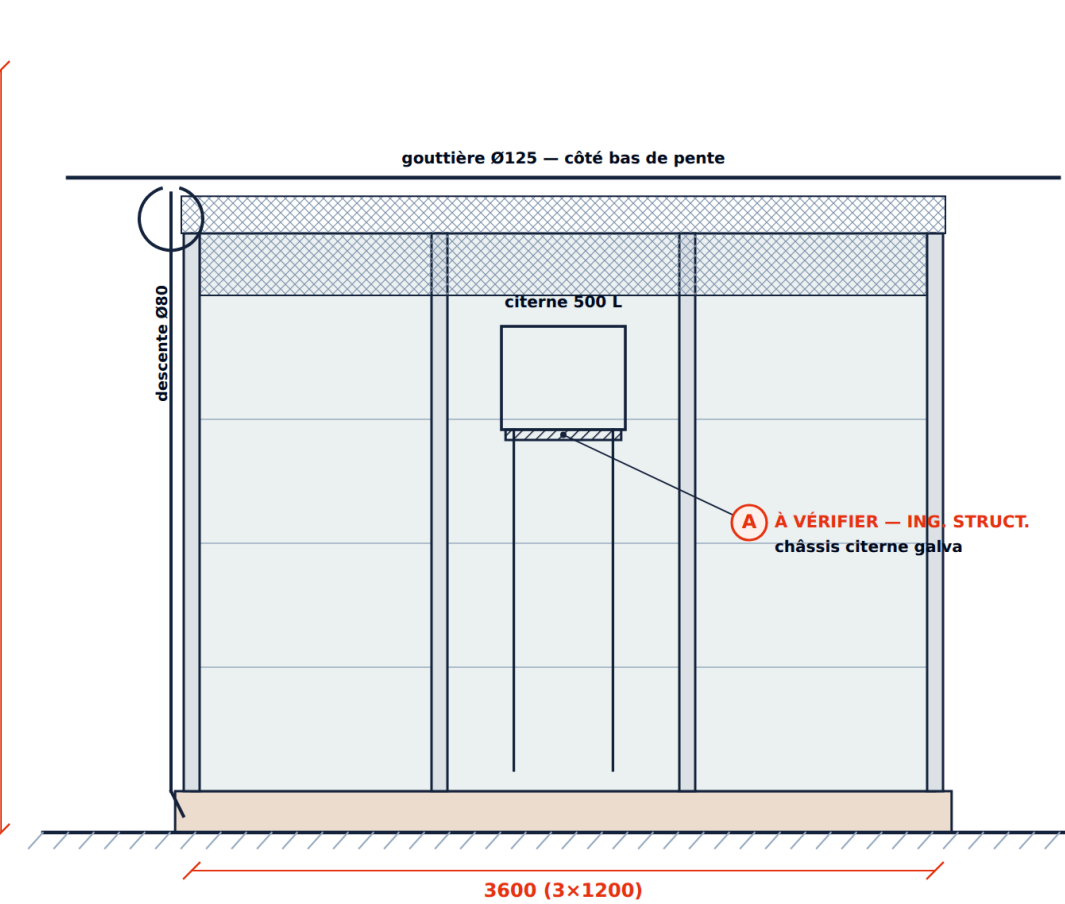

4 · COUPE PLOMBERIE — citerne → siphon → collecteur → puisard
éch. ≈ 1:22

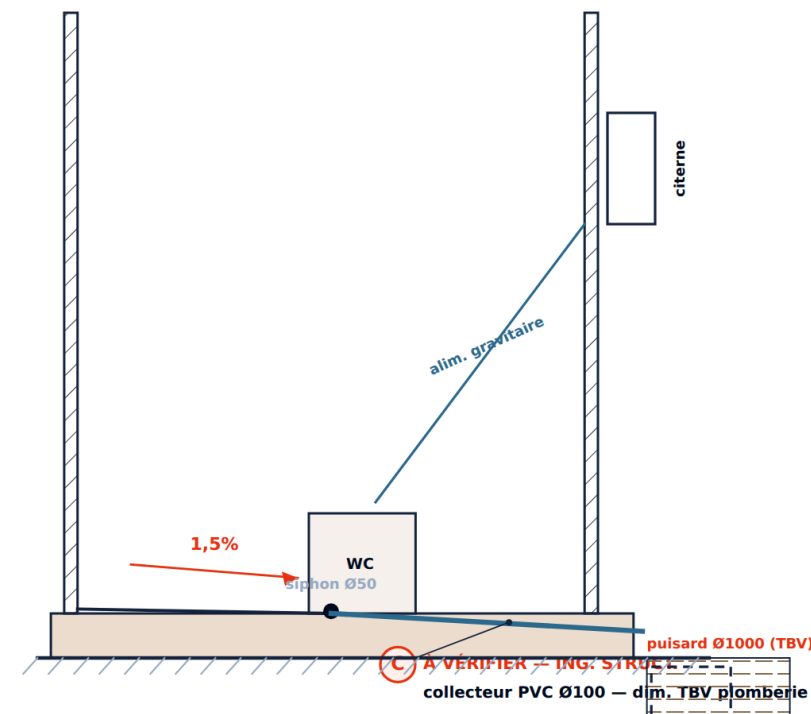


QUANTITATIF — MODULE SANITAIRE

Poteaux périm. 150×150	10
Poteaux U cloison (TBV)	2
P1 1200×600×60	40 (dont 8 cloison)
P2 claustra	10
P4 portes + impostes	2 + 2
P6 grilles basses	2
WC / lave-mains / siphons	2 / 2 / 2
Citerne 500 L + châssis (TBV)	1
Puisard Ø1000 (TBV)	1

comptes calculés depuis la géométrie (check.mjs)


1 · PLAN — 3 FENÊTRES, PORTE ARRIÈRE, GUICHET, TABLETTE

éch. $\approx 1:18$

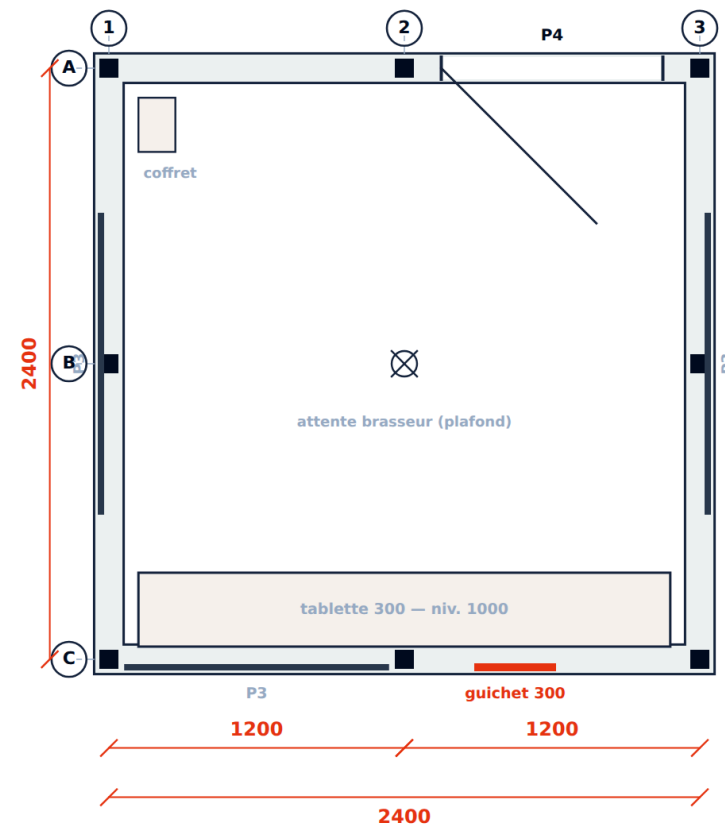


3 · DÉTAIL GUICHET — COUPE VERTICALE (réservation moulée)

éch. $\approx 1:5$

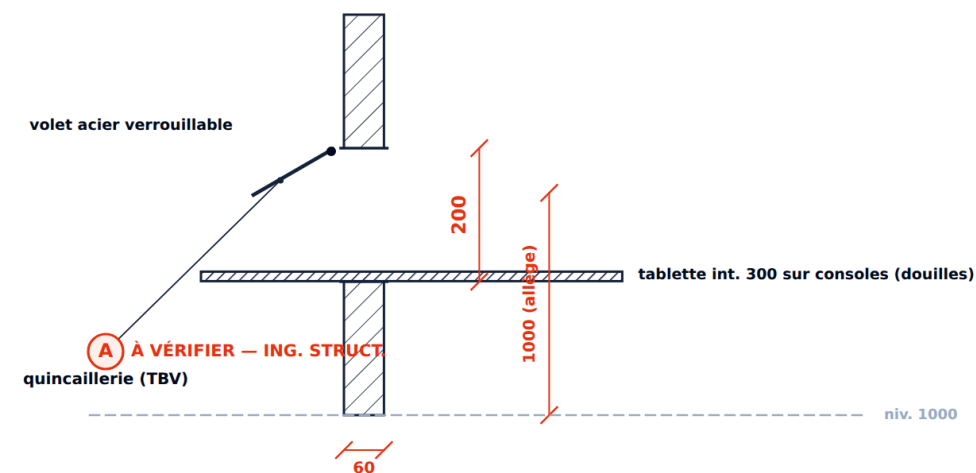


2 · ÉLÉVATION AVANT — FENÊTRE + GUICHET DANS P1G

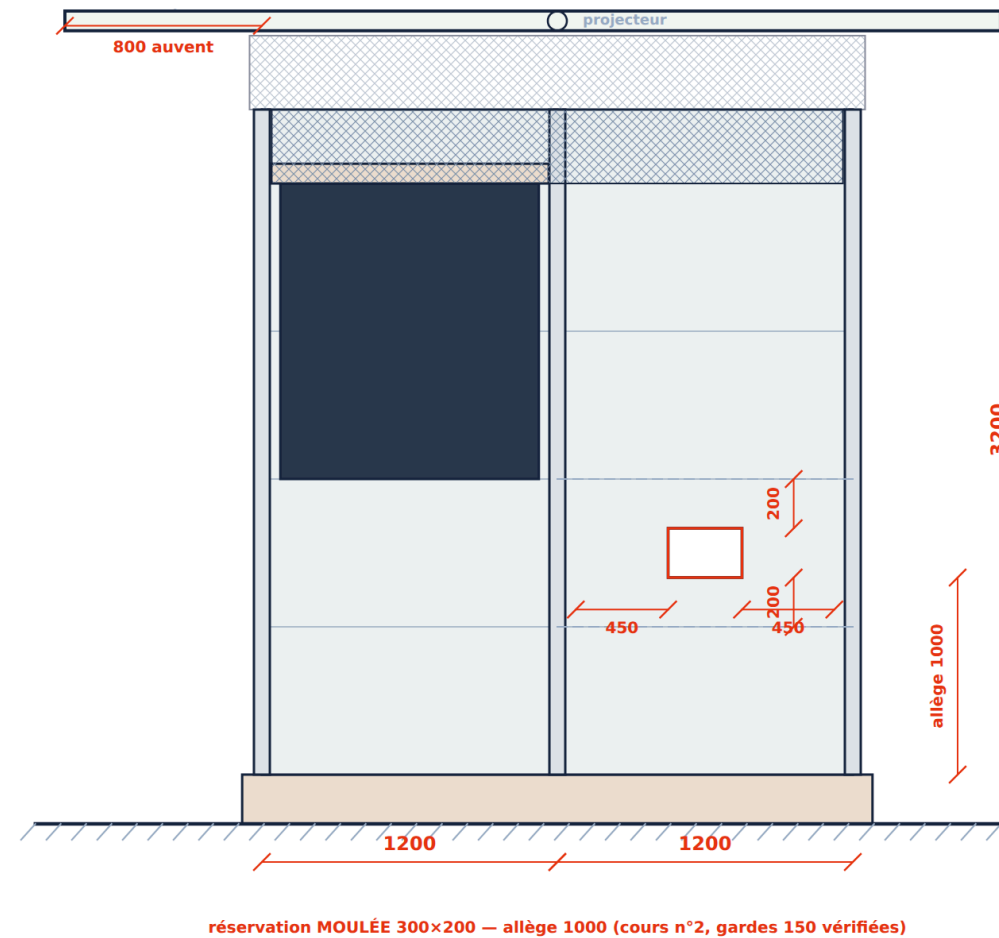

4 · SCHÉMA ÉLECTRIQUE UNIFILAIRE (M2)

sans échelle

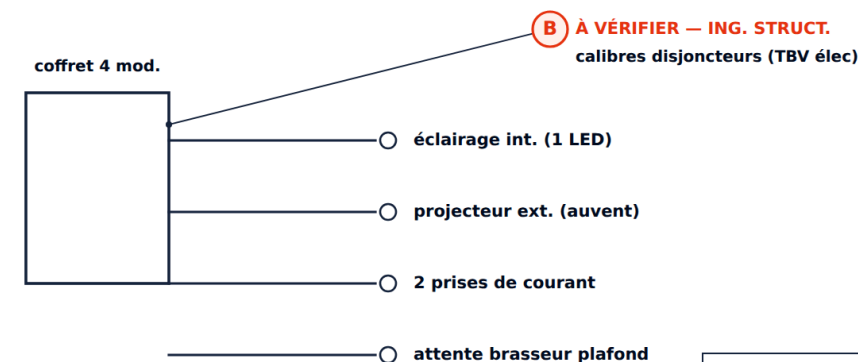

⚠ AUCUNE plomberie — module M2

QUANTITATIF — POSTE DE GARDIENNAGE

Poteaux périm. 150x150	8
P1 1200x600x60	21
P1G (réservation guichet)	1
P2 claustra	8
P3 persiennes + P5 casquettes	3 + 3
P4 porte + imposte	1 + 1
Tablette + consoles	1
Coffret + PC + LED + projecteur	1+2+1+1