

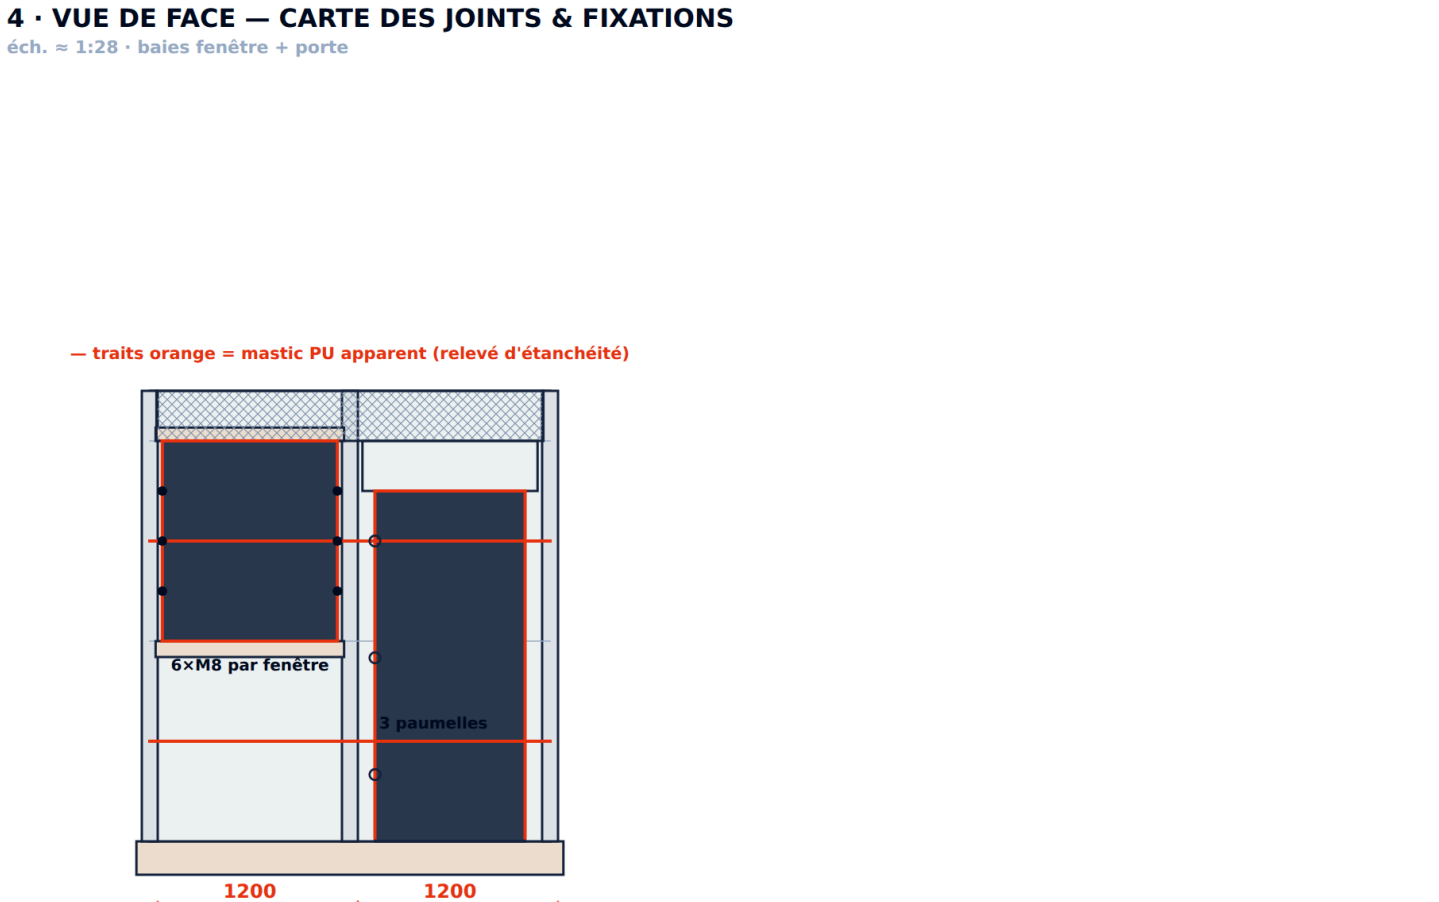
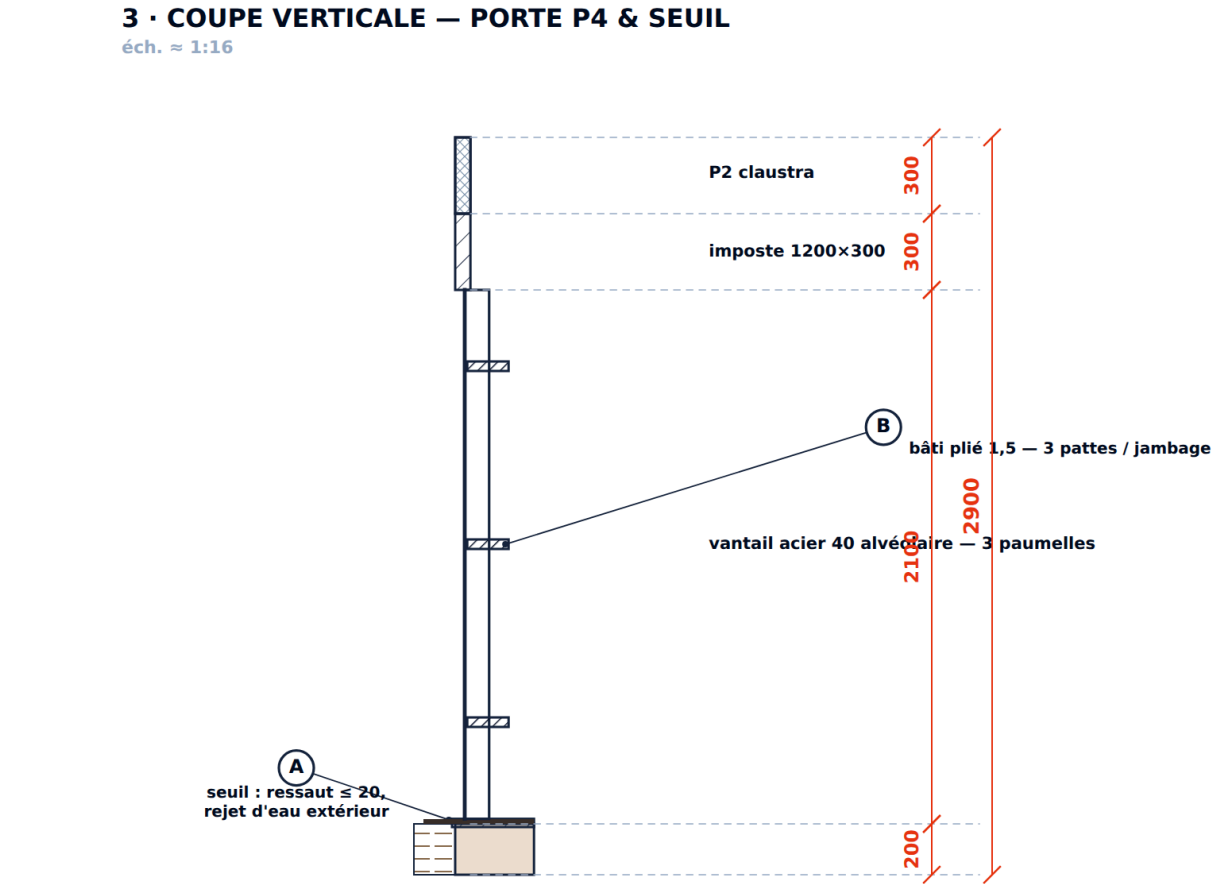
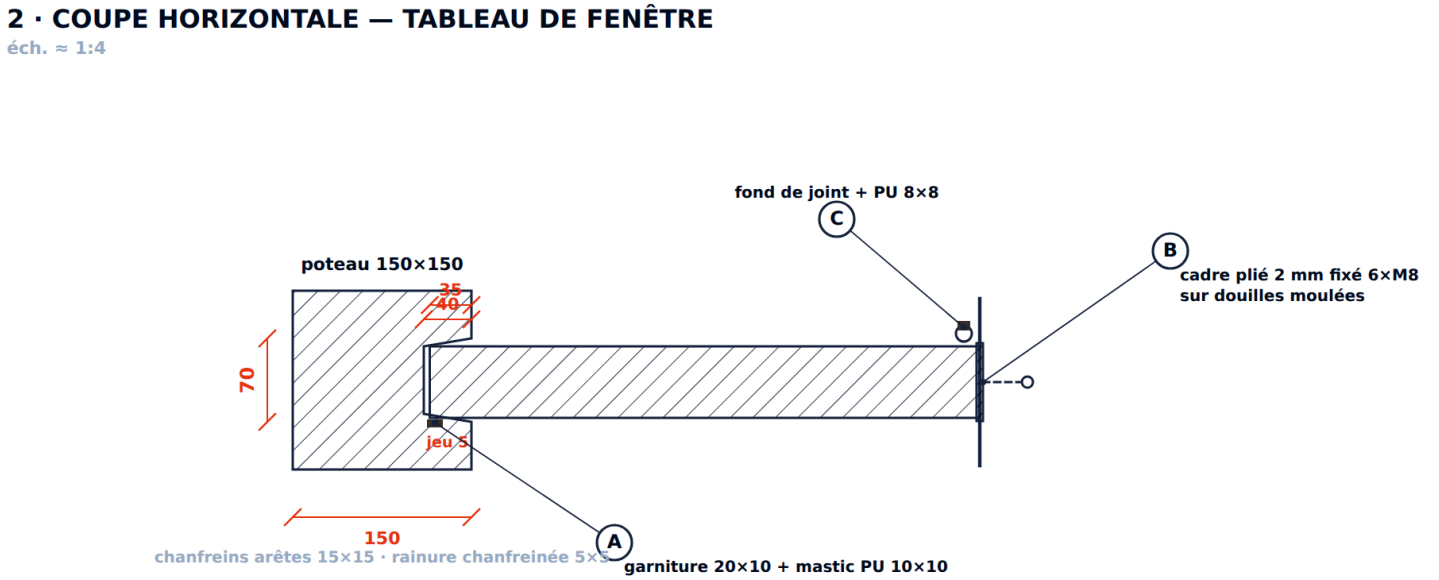


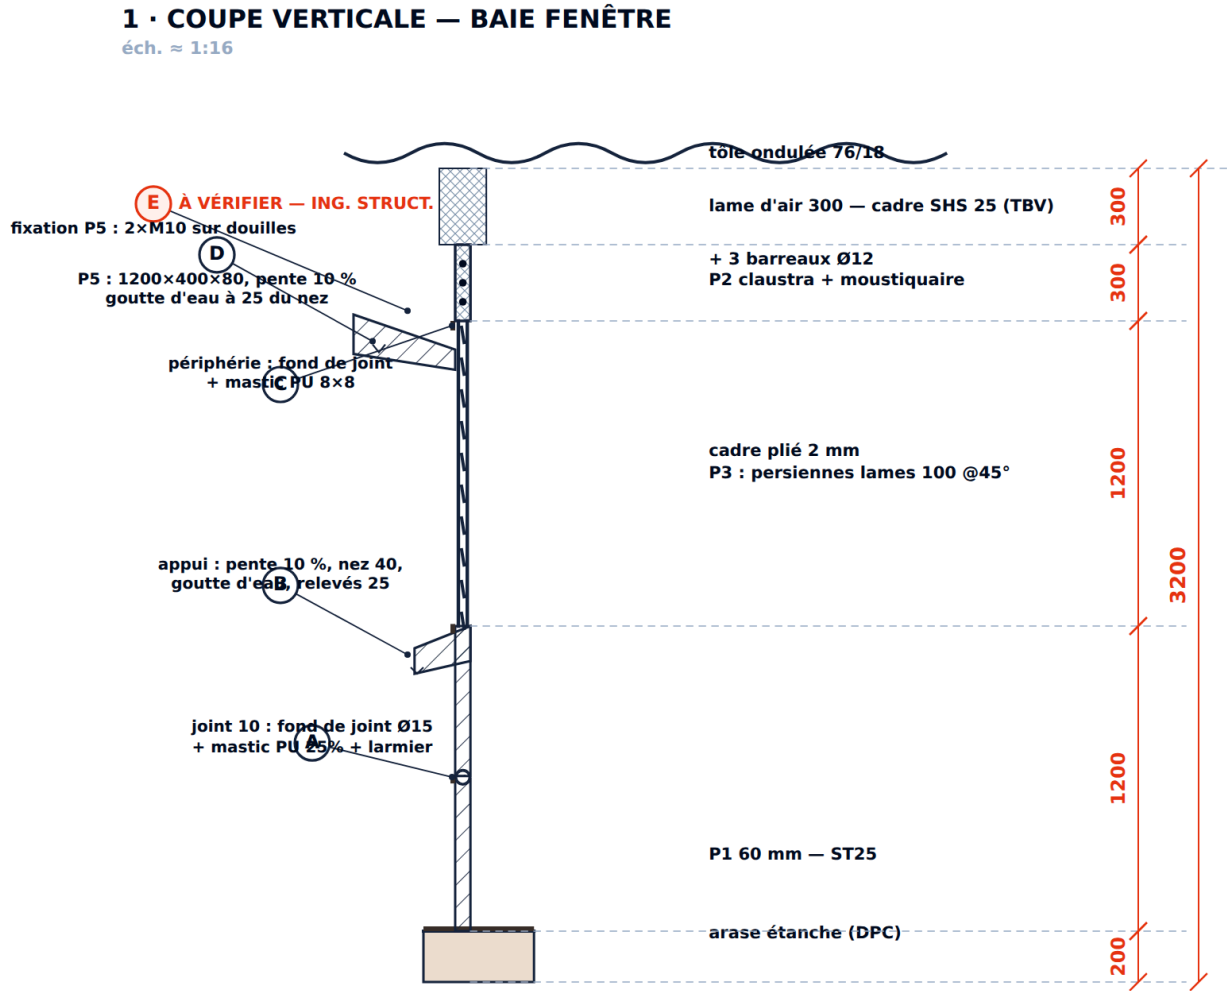


1 · COUPE — TÊTE DE POTEAU / ÉQUERRE / PANNE

éch. ≈ 1:6

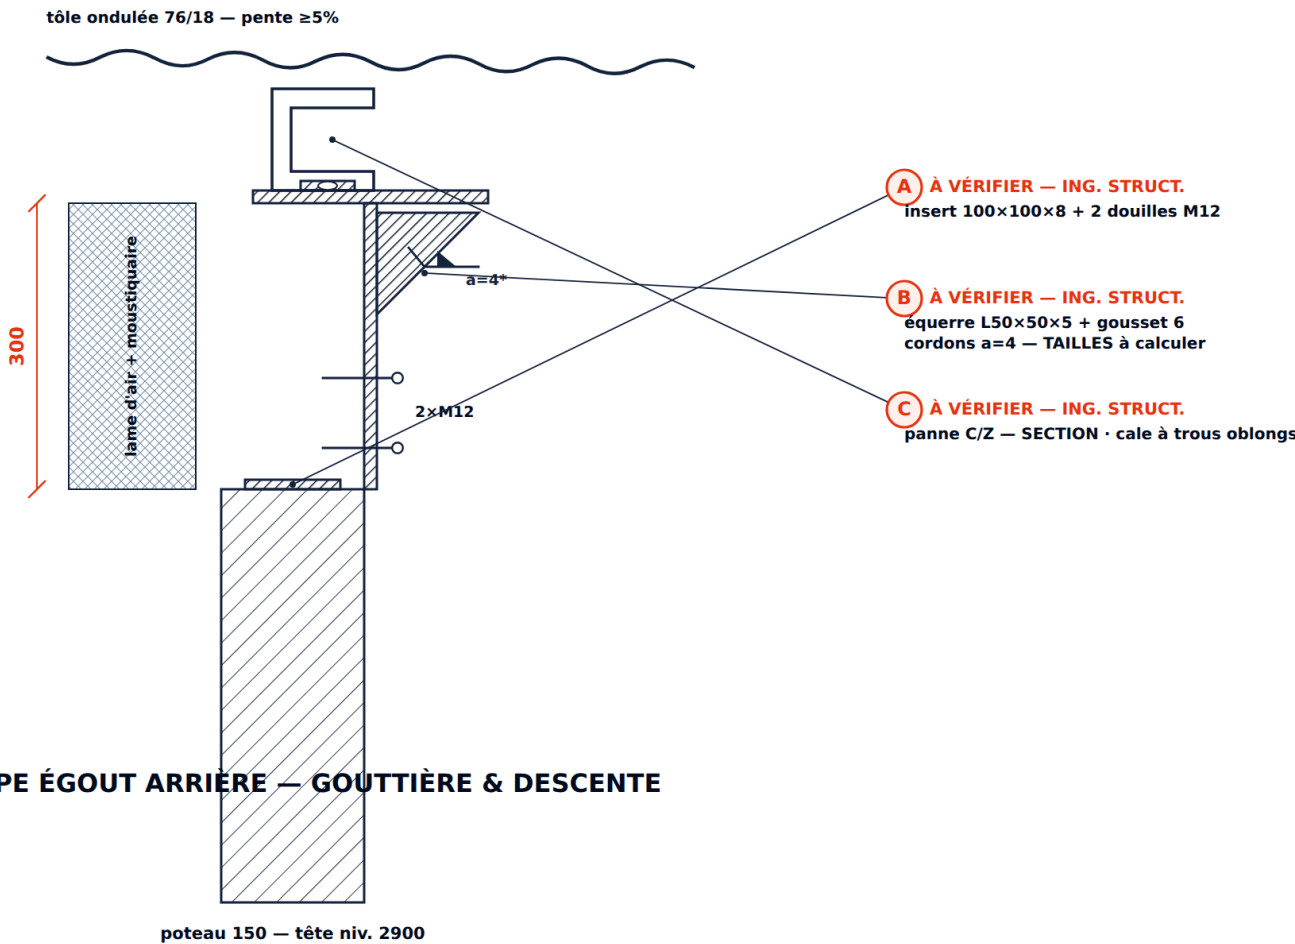


3 · COUPE ÉGOUT ARRIÈRE — GOUTTIÈRE & DESCENTE

éch. ≈ 1:8

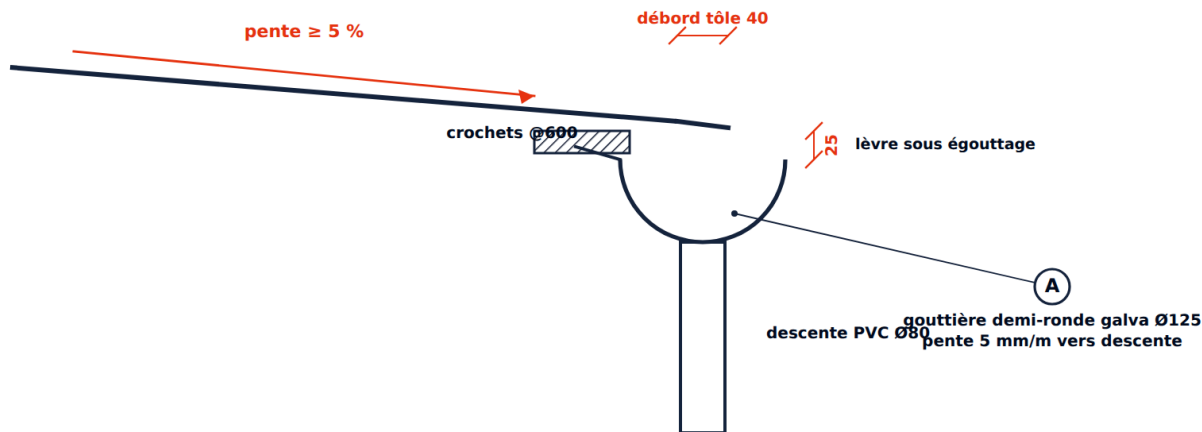


2 · FIXATION TÔLE — VIS EPDM & DENSITÉS

éch. ≈ 1:2 / schéma

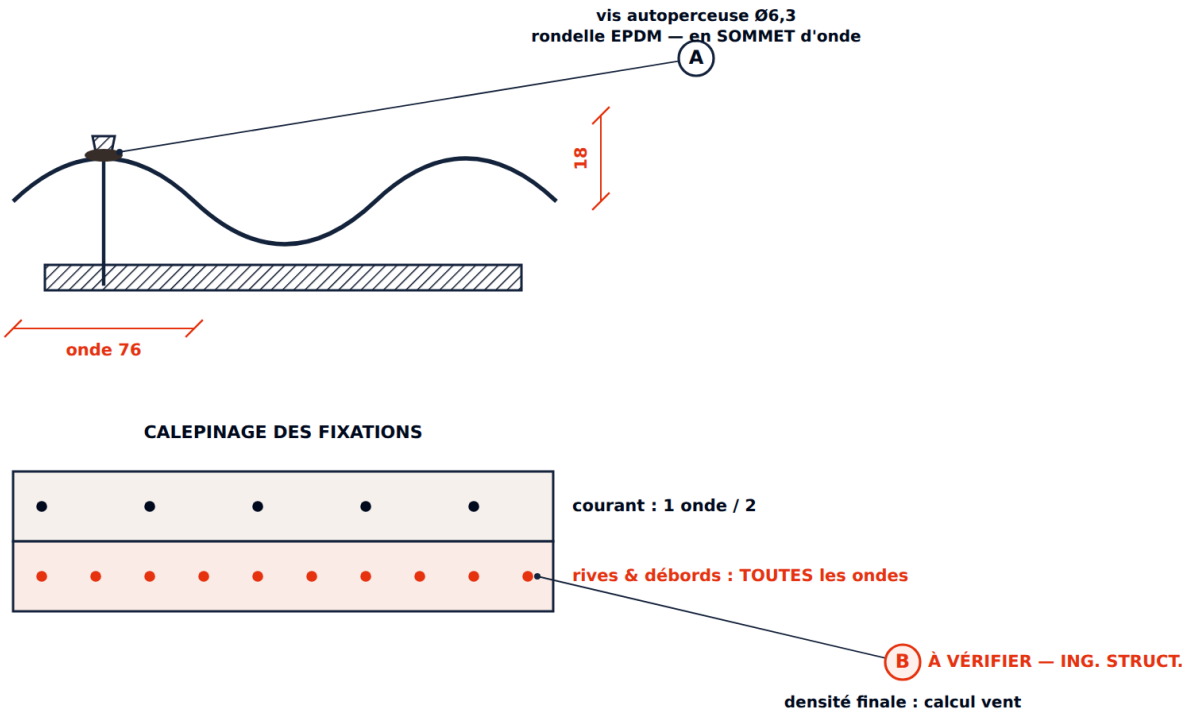


4 · PLAN DE TOITURE — ÉQUERRES, PANNES, ZONES DE FIXATION

éch. ≈ 1:56

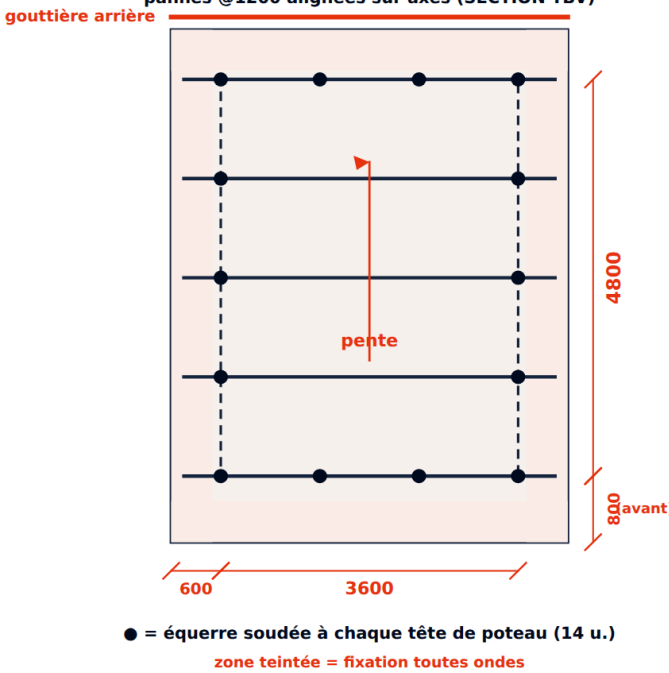


1 · COUPE HORIZONTALE — POTEAU RAINURÉ + 2 PANNEAUX

éch. ≈ 1:3

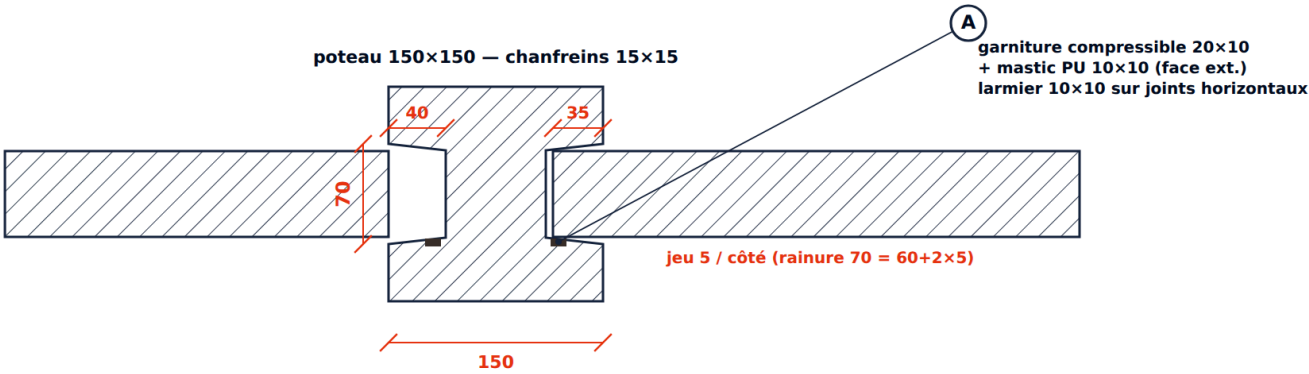

2 · COUPE VERTICALE — LINTEAU P9 SUR APPUIS + COFFRE RIDEAU

éch. ≈ 1:13

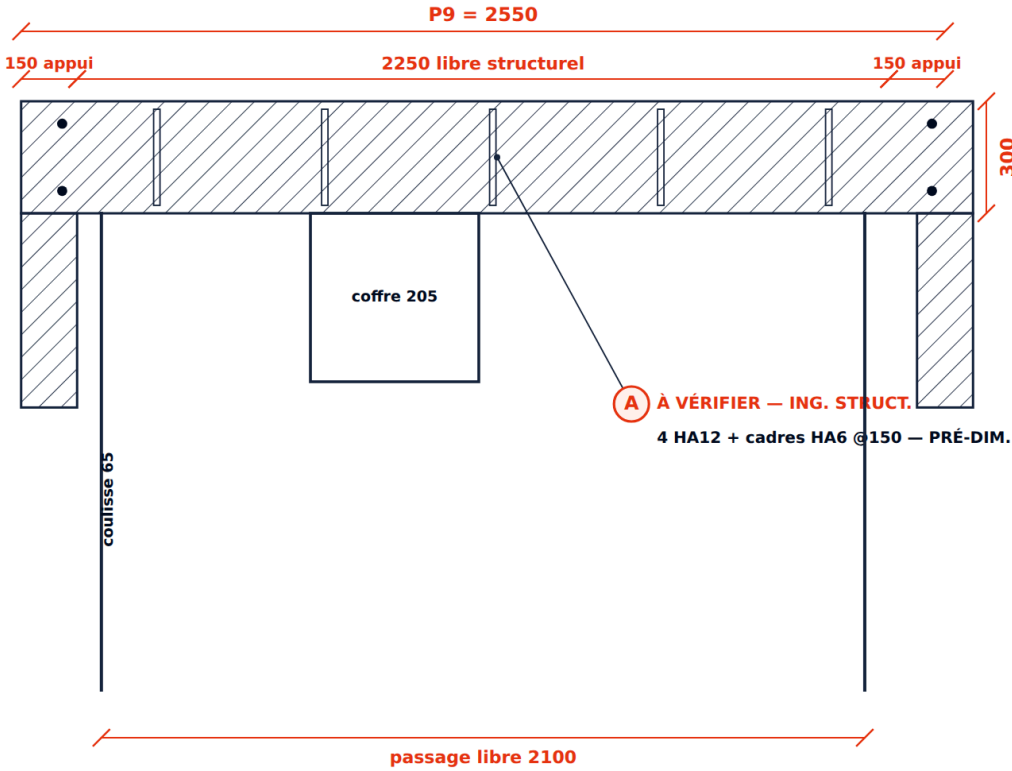


masse P9 ≈ 275 kg — méthode de pose À VÉRIFIER (pose à 6 ou levage léger)

3 · BASE VARIANTE LOCATION — SKID DÉMONTABLE


éch. ≈ 1:9

5 traverses (1 par ligne de poteaux) + 2 longerons — ensemble DÉMONTABLE

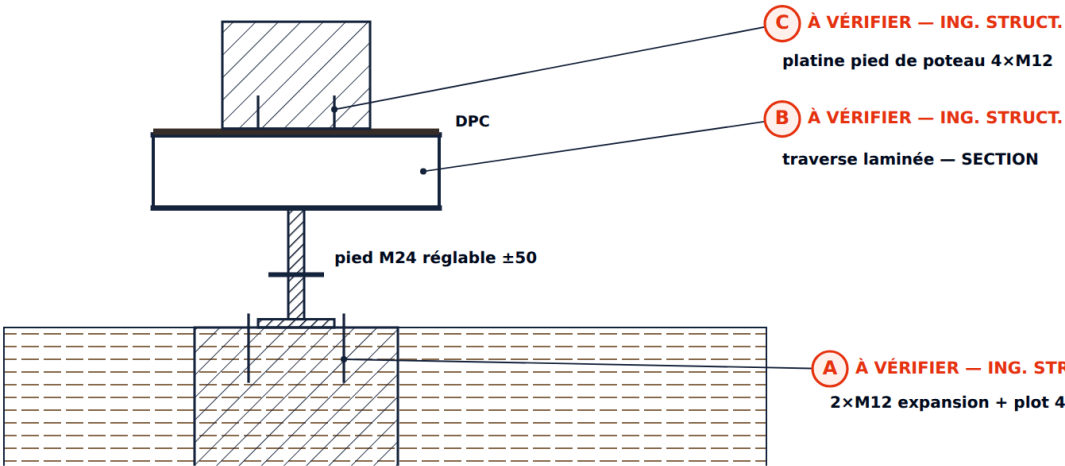

4 · BASE VARIANTE VENDU — SCÉLLEMENT + DALLE

éch. ≈ 1:9

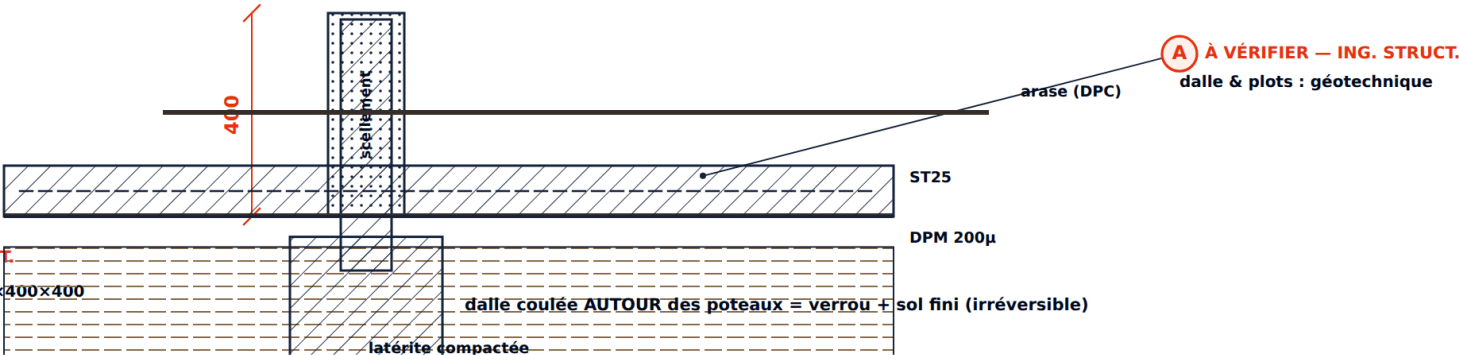

NOMENCLATURE P1→P9

P1	1200×600×60	104 kg	béton C25/30 + ST25
P2	1200×300×60	32 kg	béton + moustiquaire + 3Ø12
P3	1200×1200	35 kg	persiennes acier 2 mm
P4	900×2100+imposte	55 kg	acier plié 1,5 / vantail 40
P5	1200×400×80	88 kg	béton, pente 10%
P6	600×200×60	12 kg	béton + moustiquaire
P7	1200×600	—	plafond composite (PL. ult.)
P8	kit technique	—	citerne + coffret (PL. ult.)
P9	2550×300×150	275 kg	béton armé — TBV